

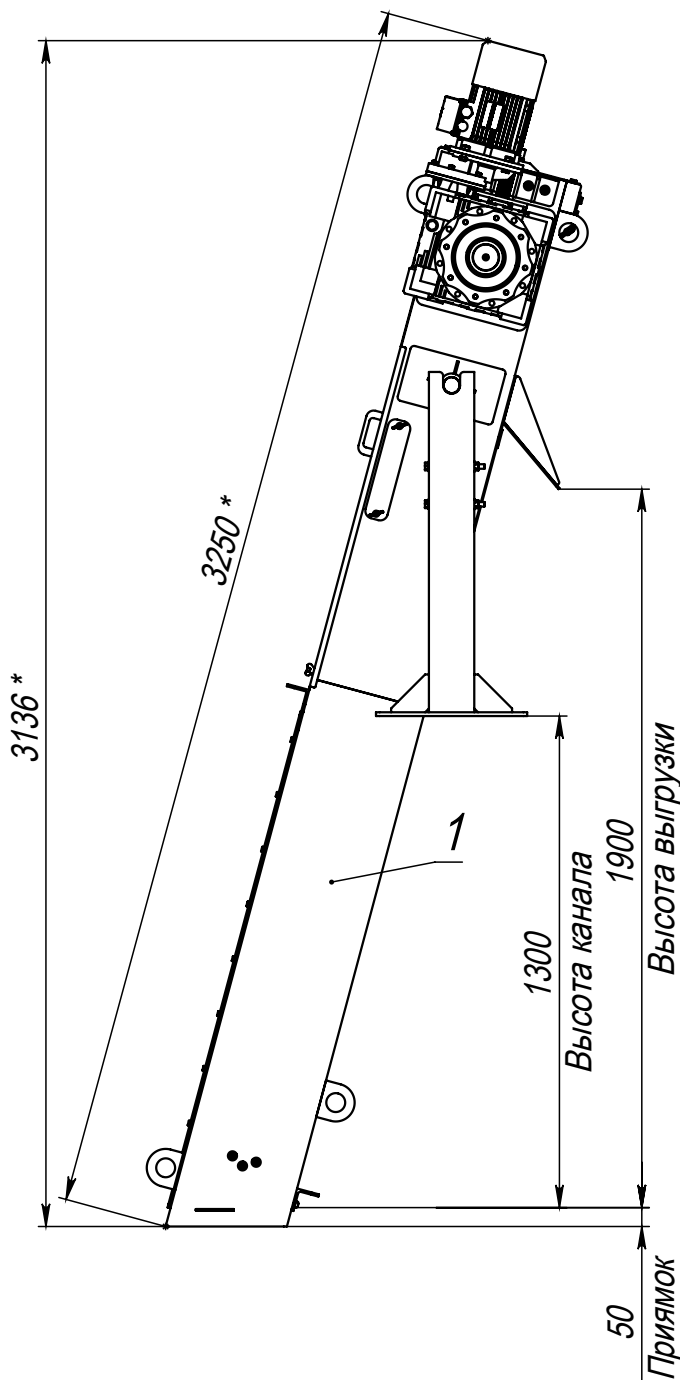


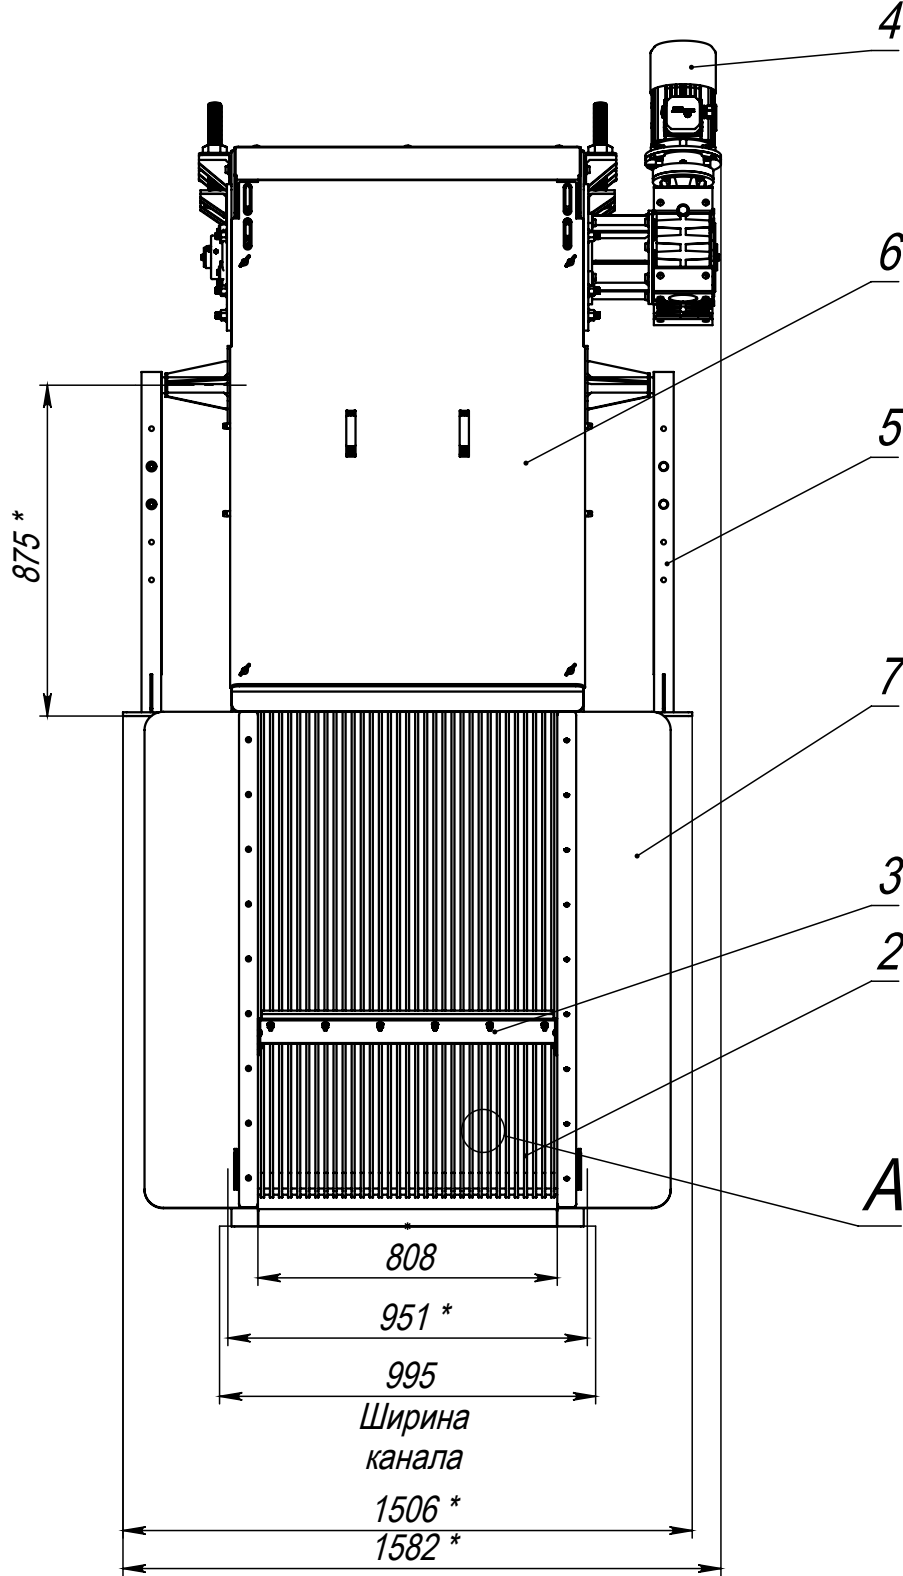

A (1 : 5)

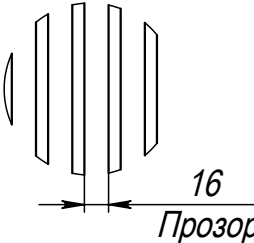

- 1. *Размер для справок
- 2. Уплотнение для монтажа в канал поставляется с решеткой
- 3. Возможно изменение конструкции после прочностных расчетов
- 4. Запрещается вносить правки на листе согласования без согласования с разработчиком

№	Наименование	Кол-во	Примечание
1	Каркас	1	AISI 316
2	Экран	1	AISI 316
3	Граблина	8	AISI 316
4	Электропривод	1	1,1 кВт
5	Опора	1	Сталь 3
6	Крышка	1	AISI 316
7	Уплотнение в канал	2	EPDM

					Решетка грабельная Vökker						
					GR-PR16-VM1900 1300x995	Лит.			Масса	Масштаб	
Изм.	Лист	№ докум.	Подп.	Дата						1:20	
Разраб.	Беляева										
Пров.	Кунтушев										
Т. контр.											
						Лист			Листов 1		
Н. контр.						ООО "Тех-Аэро"					
Утв.	Кунтушев										

Согласовано.
Покупатель: _____
наименование организации

_____ / _____
подпись расшифровка

"__" ____ 20__ г.

Согласовано.
Поставщик: _____
наименование организации

_____ / _____
подпись расшифровка

"__" ____ 20__ г.